



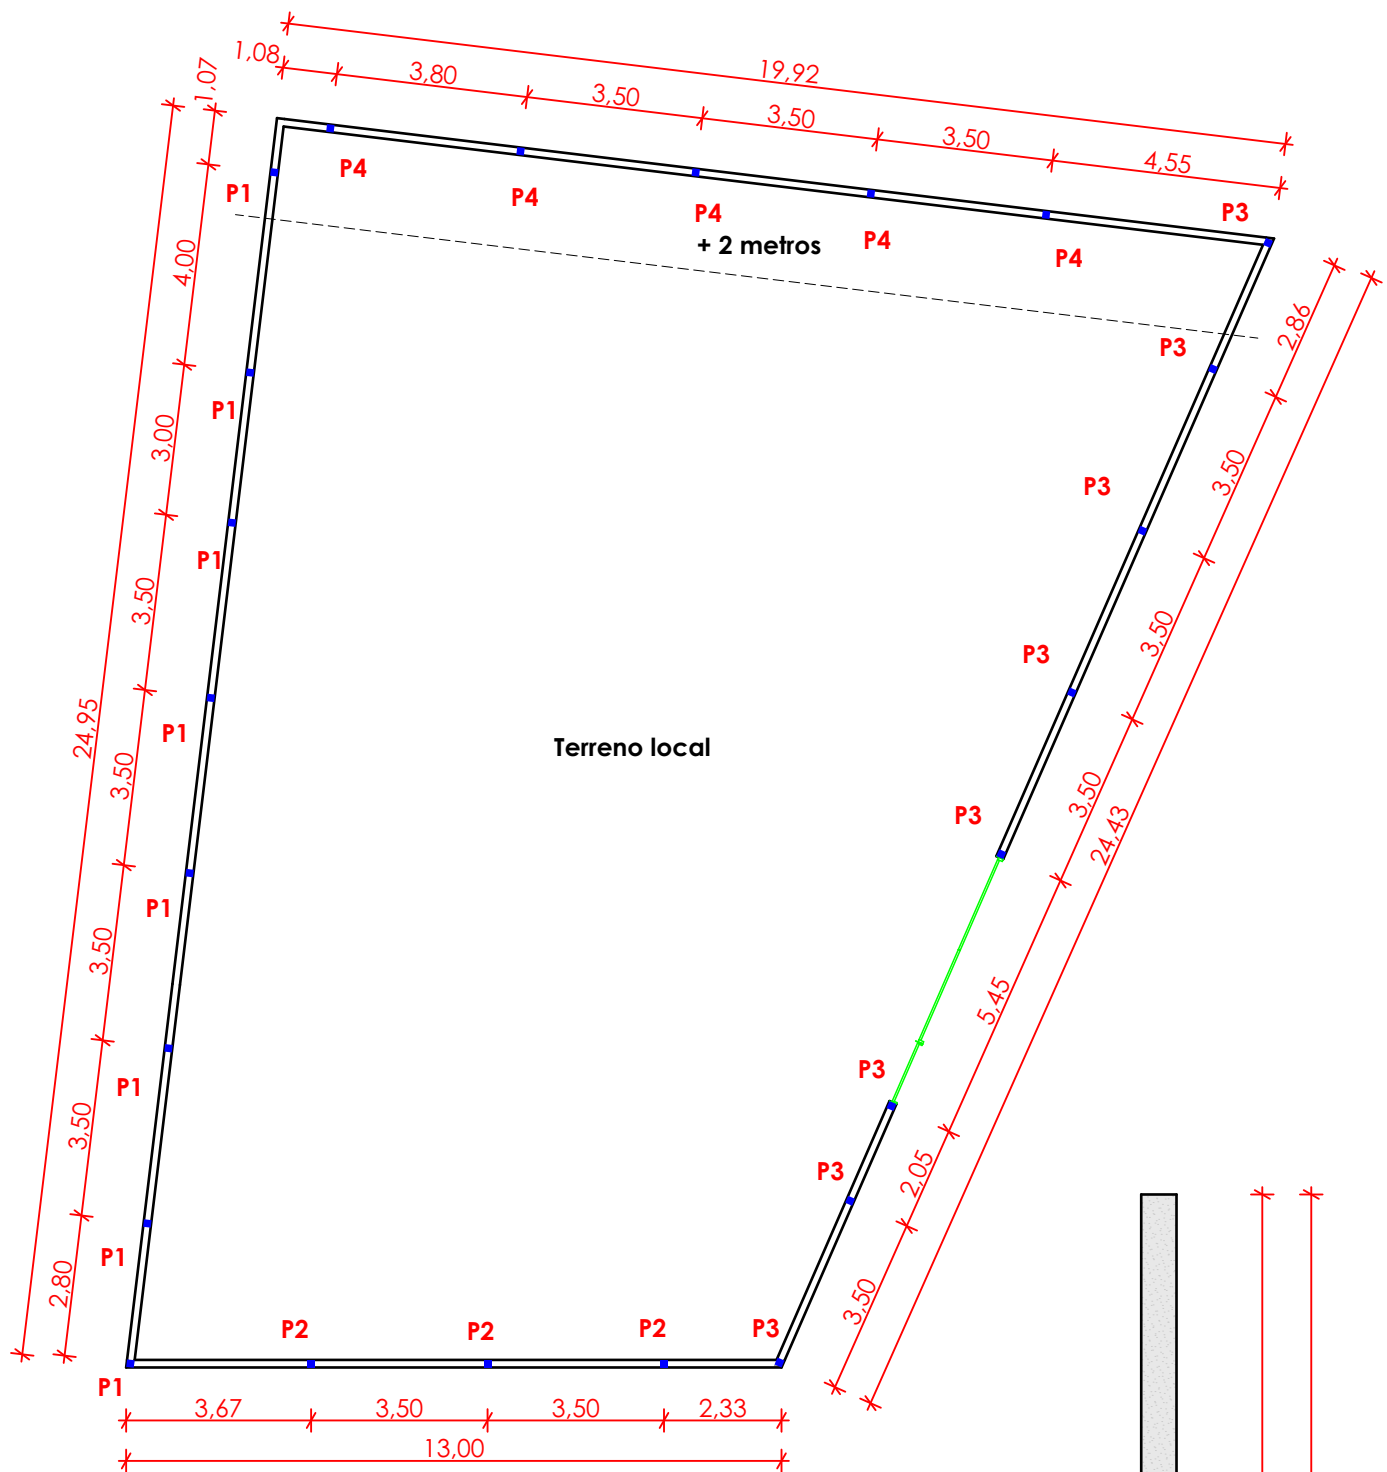

* 13 fiadas
em cima

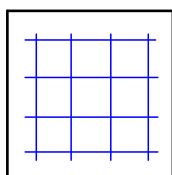

*ferro 10 @15cm

*Sapata 60 por 60 por 20 cm


*ferro 6 @15cm
* 4 ferros 10



*Viga de cima 15 por 20

*Pilar 15 por 15

* 5 fiadas
bloco + betão

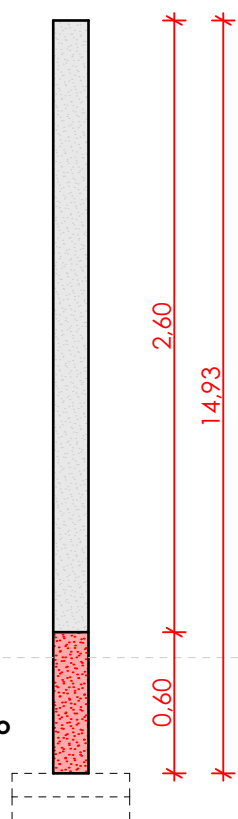

*5 cm betão de limpeza
*10 cm de enrocamento